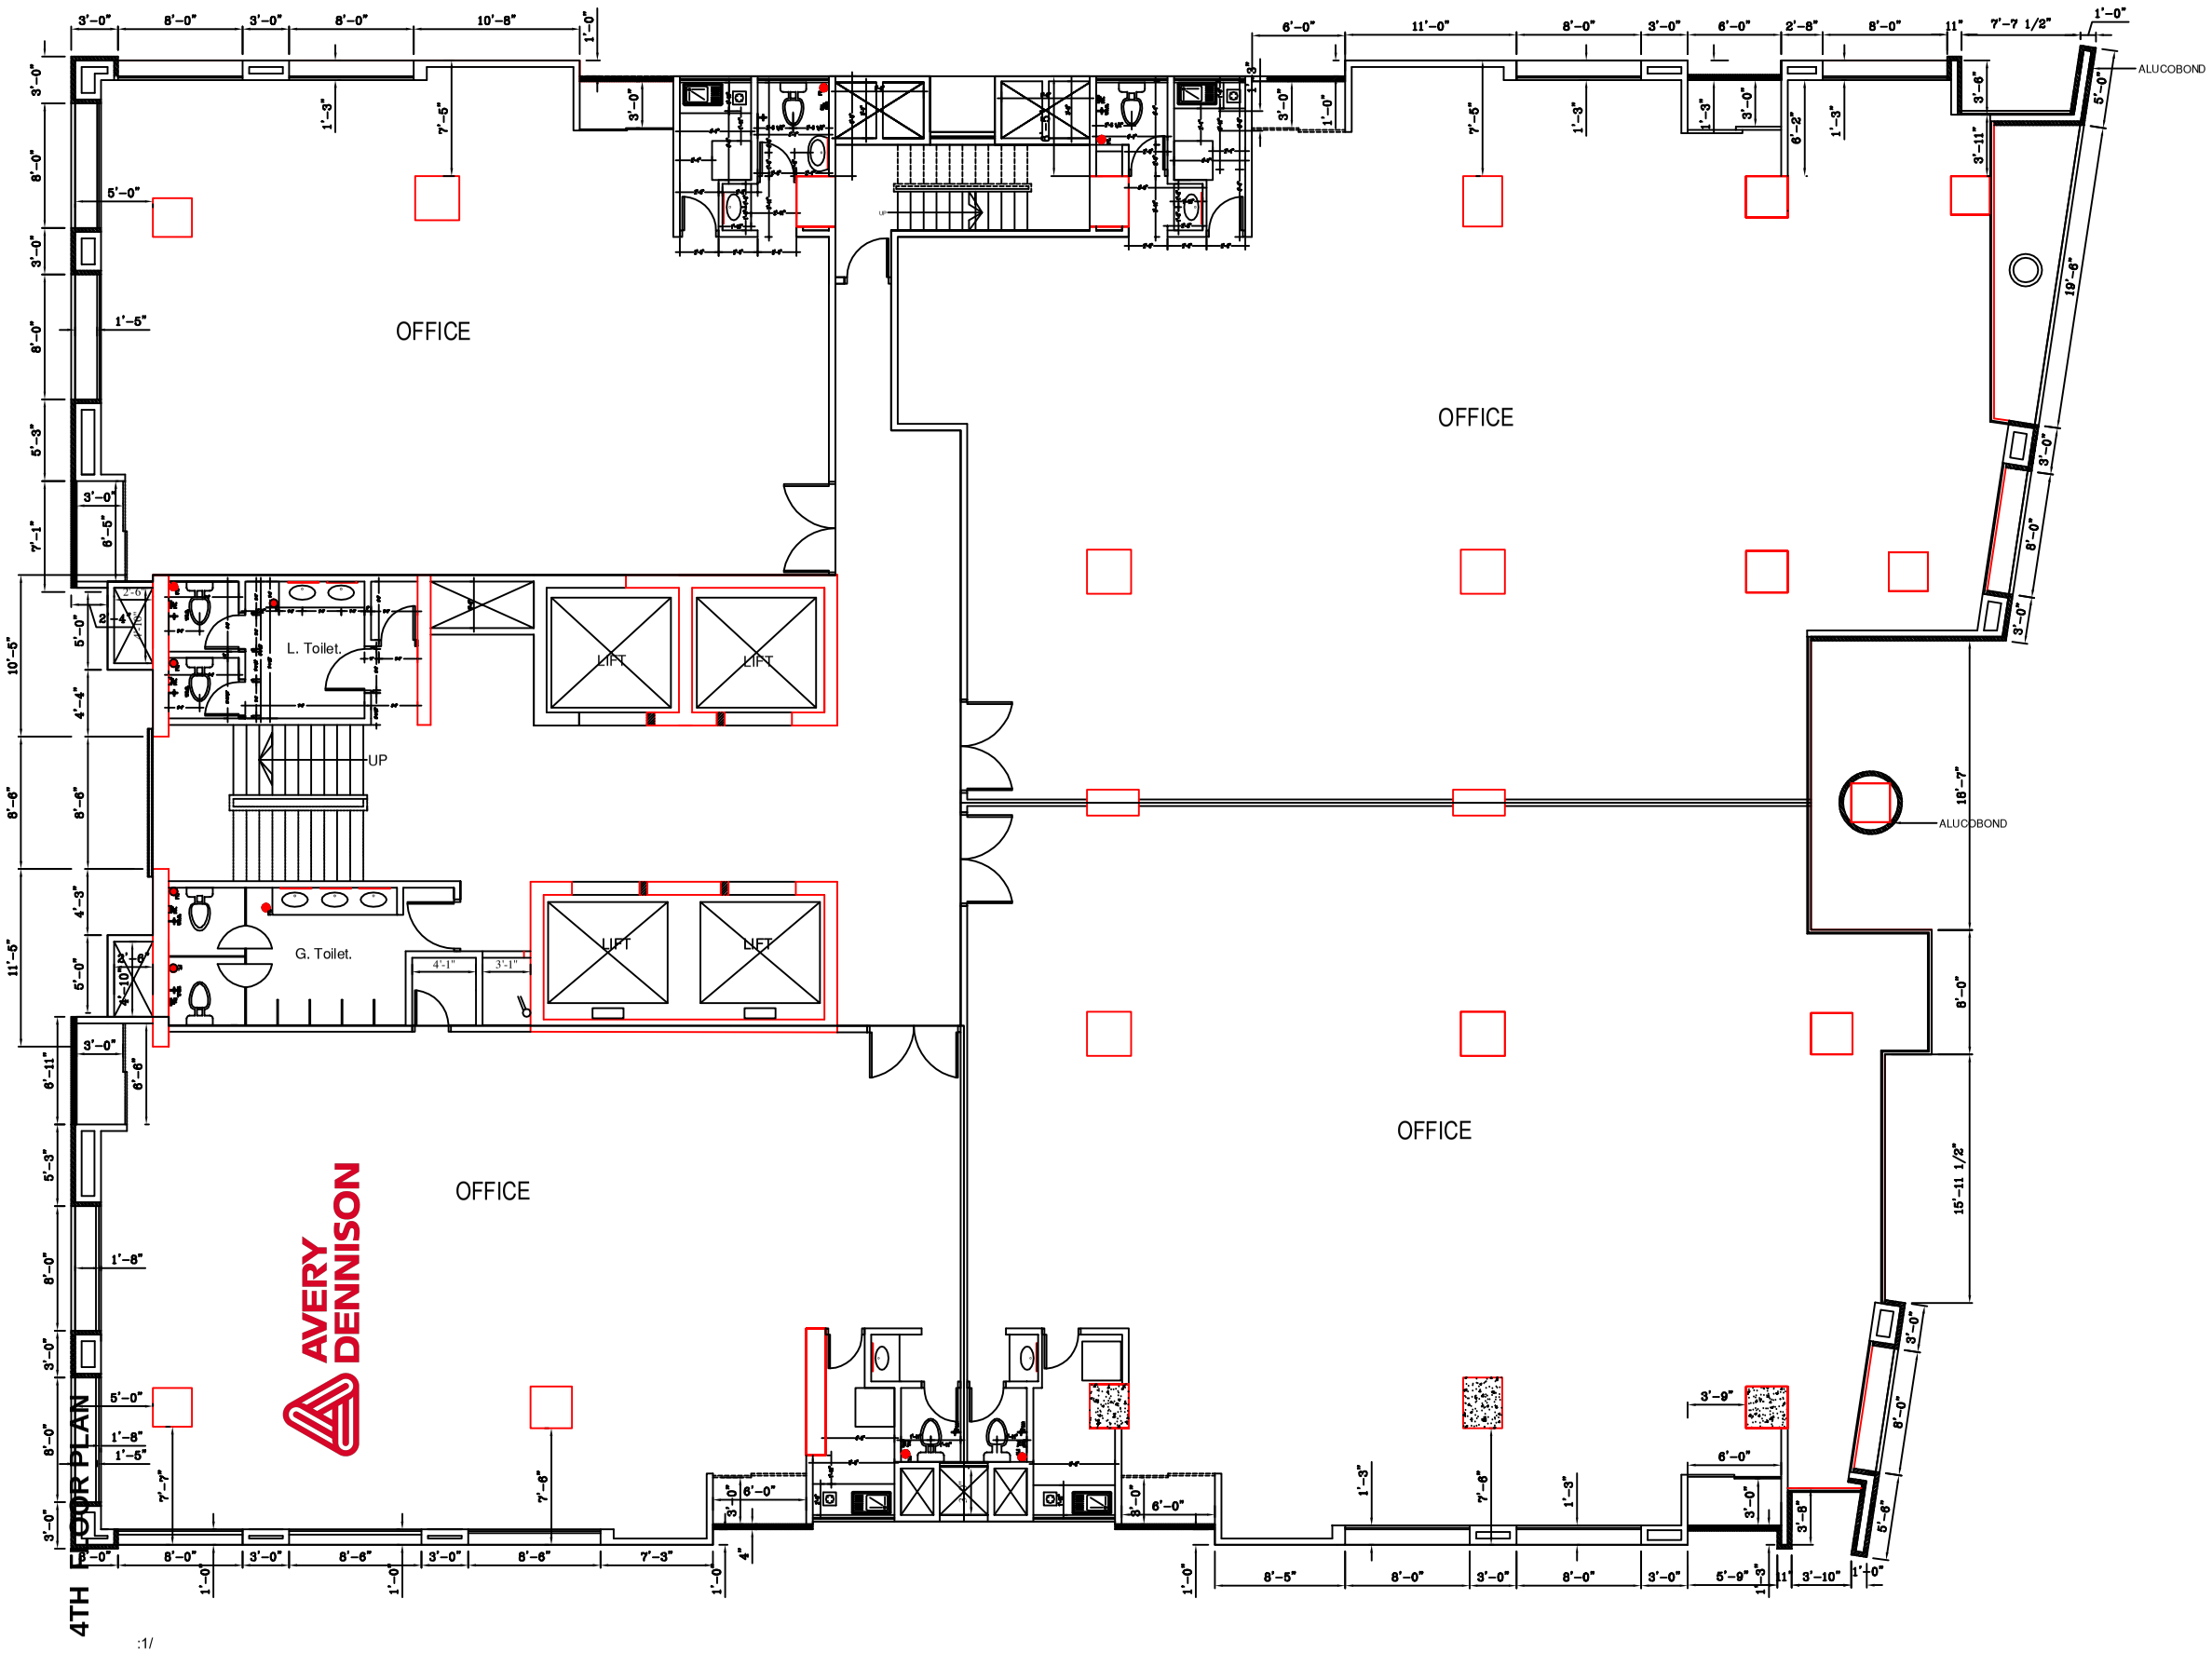


GENERAL INSTRUCTION

1) THIS IS A COMPUTER AIDED DRAWING DO NOT AMEND ANY PART MANUALY.
2) CONTRUCTOR SHOULD VERIFY ALL THE DIMENSIONS PRIOR TO CONSTRUCTION.
3) ALL THE DIMENSIONS ARE IN FEET & INCH.
4) DO NOT SCALE THIS DRAWING, USE FIGURED DIMENSION ONLY.
5) IF THERE IS ANY CONFUSION REGARDING ANY ASPECTS OF THE DRAWING, PLEASE CONSULT THE SUPERVISING ARCHITECTS & ENGINEERS.
6) EXISTING GROUND LEVEL (E.G.L.) IS CONSIDERED REFERENCE LEVEL AS 0'-0"
7) THIS DRAWING IS A PROPERTY OF INTERDEC SYSTEMS ANY REPRODUCTION OF THIS DRAWING MUST BE DONE WITH PRIOR WRITEN PERMISSION FROM INTERDEC SYSTEMS.

PROJECT NAME:

22 STORIED COMMERCIAL COMPLEX BUILDING WITH 04-LEVEL BASEMENT AT 57& 57/A,GULSHAN AVENUE, CIRCLE-1

CLIENT:

Al-Amin Construction Co.Ltd (METRO GROUP)

ARCHITECT:

01) K.M. MAHFUZUL HUQ
02) HAROON SADI.

DRAWN BY

MD. MOFIZ UDDIN

ELECTRO MECHANICAL CONSULTANT:

DESIGN & CONCEPTS LTD.

AMENDMENT:

SL. NO.		DATE.

DRAWING TITLE:

4TH FLOOR PLAN (OFFICE)

INTERDEC SYSTEMS
Architects, Engineers, Interior Designers & Planners
HOUSE#06, ROAD#09 (GR. FLOOR),GULSHAN, DHAKA-1212,
TEL. 8825907,9889046,9889047, FAX,9890734
Email: aniqa@dhaka.agni.com

CAD FILE NO.

DATE: 24-07-2003

SHEET NO.0

ID/MGH-A008